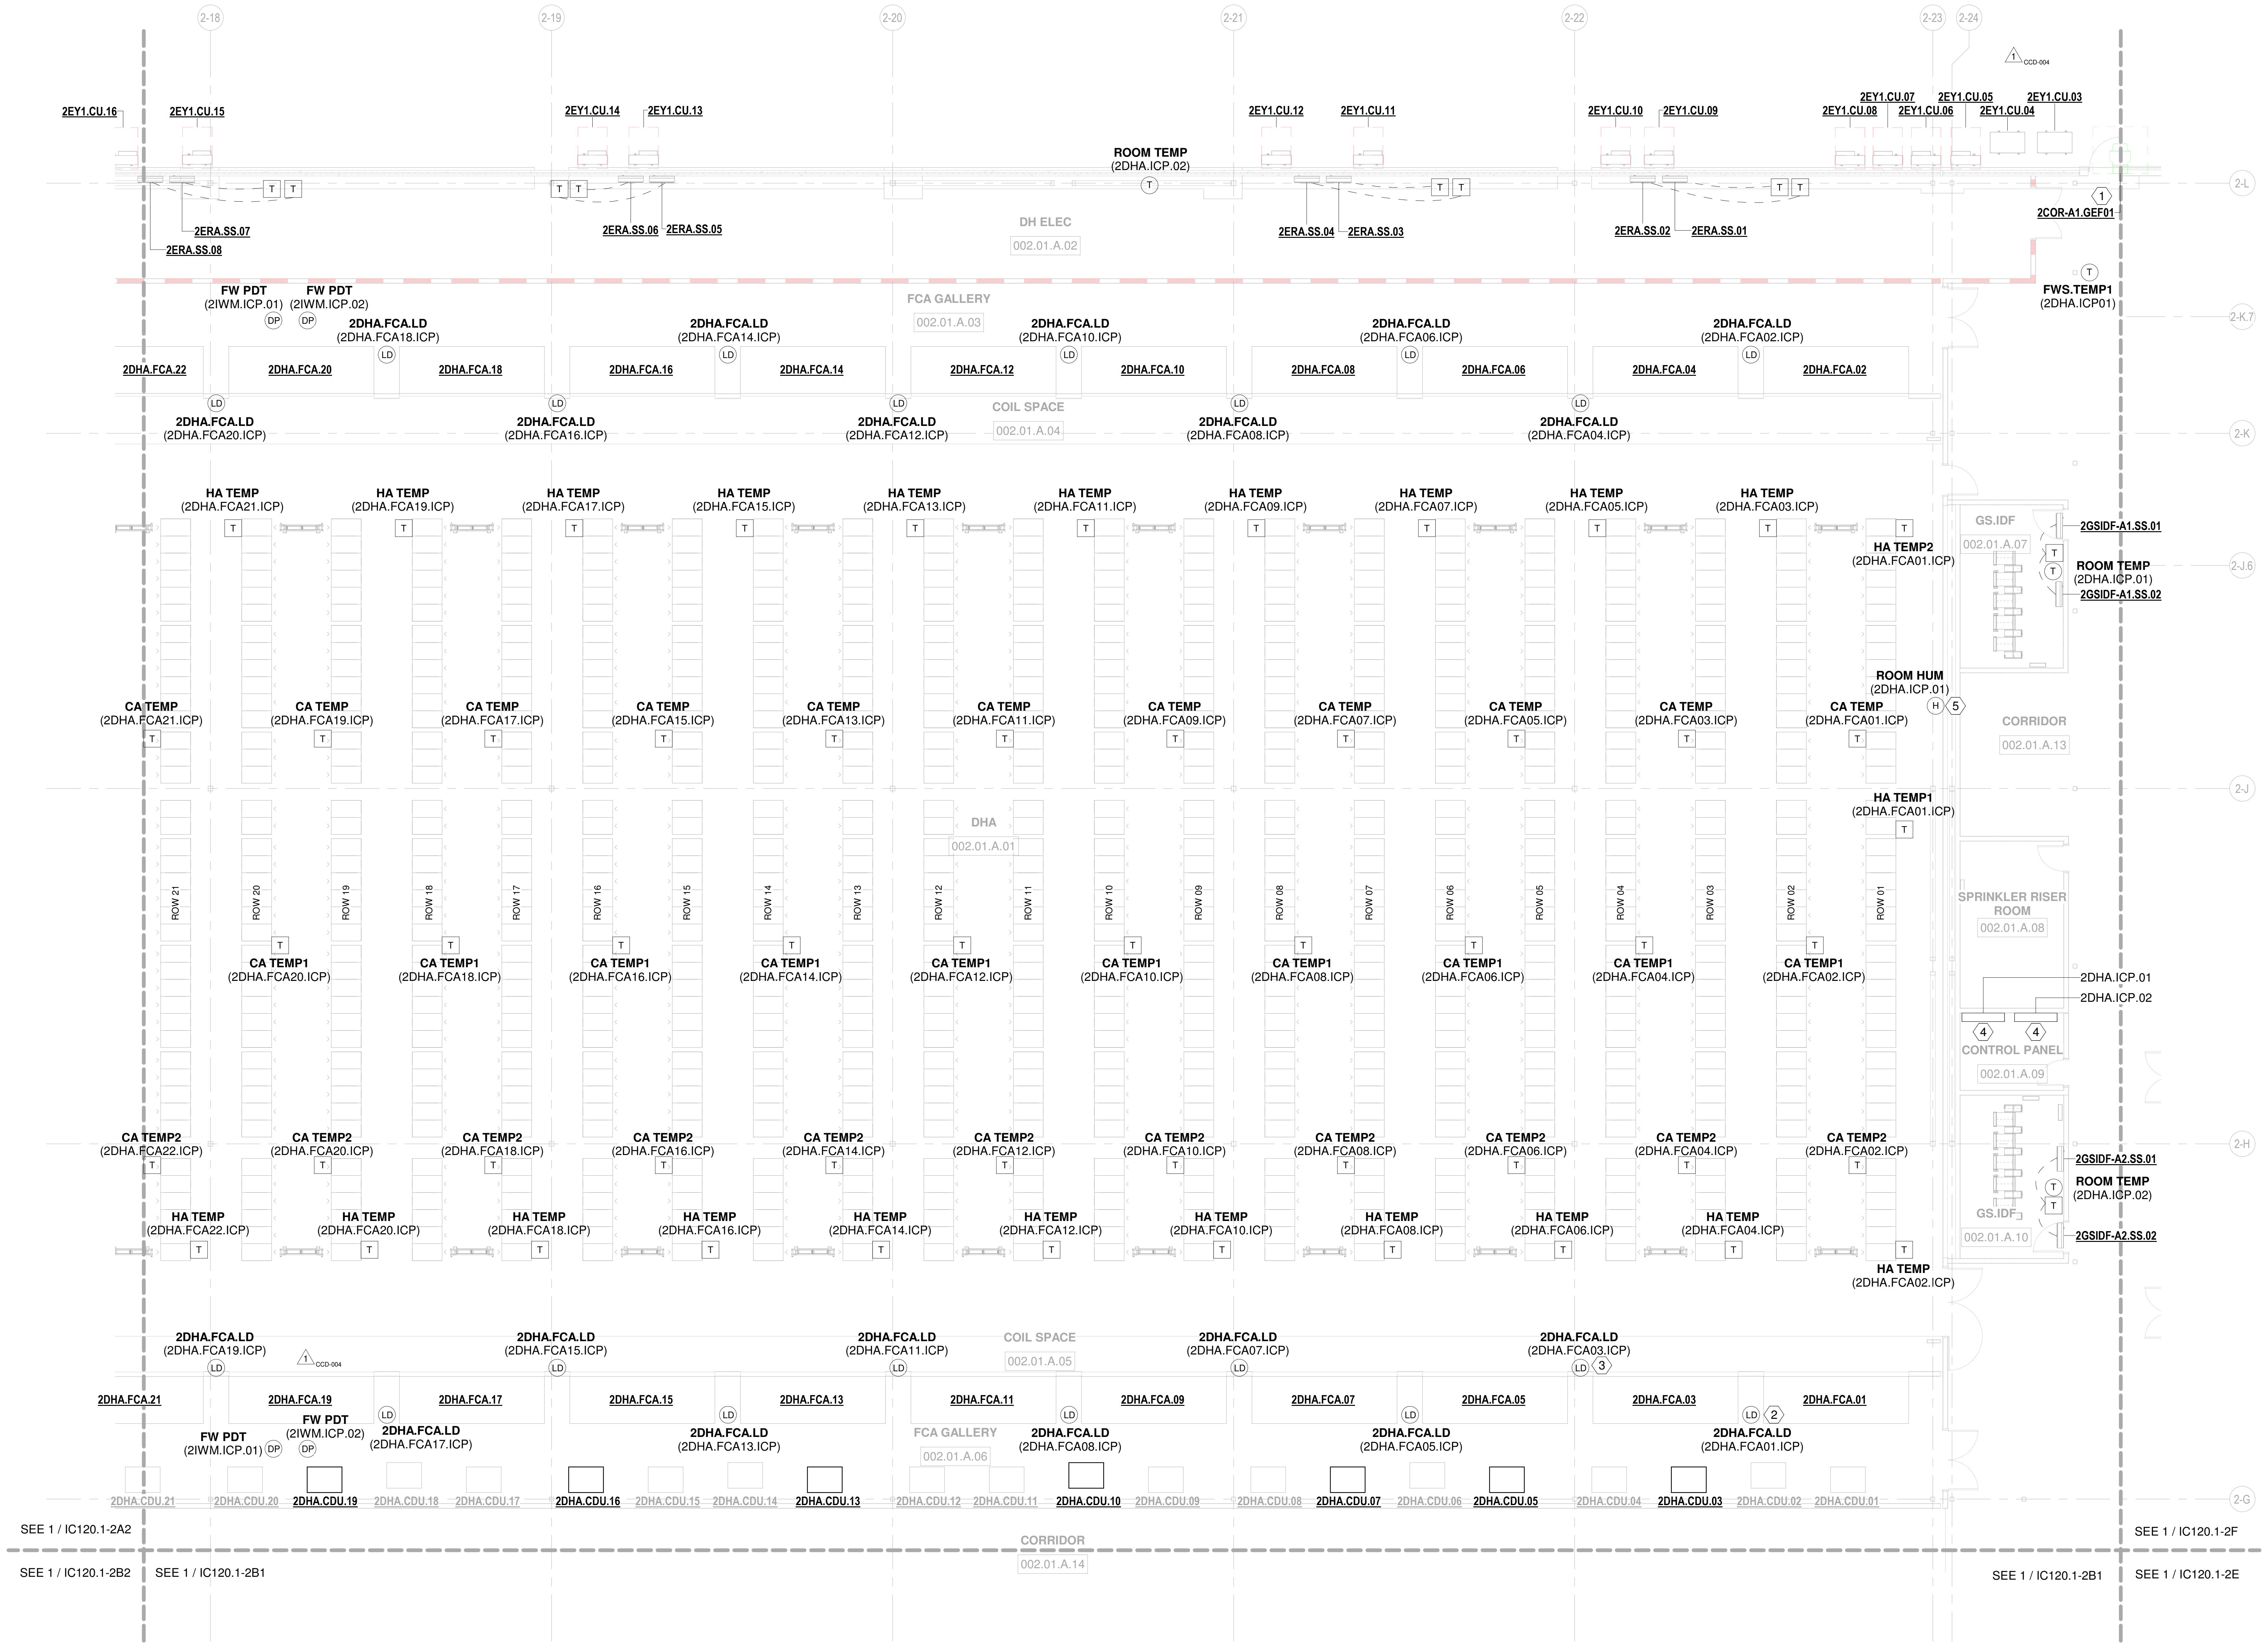

GENERAL NOTES

1. TEMPERATURE TRANSMITTERS ON EXTERIOR WALL TO BE INSTALLED WITH INSUALATED BACKING BY CONTRACTOR.
2. REFERENCE EQUIPMENT DETAILS PAGE FOR VENDOR AND CONTRACTOR RESPONSIBILITIES.
3. THE GRAY SCALED UNITS ARE DAY 2 INSTALL AND COMMISSIONING.

SHEET NOTES

NOTE: NOT ALL SHEET NOTES BELOW MAY BE USED ON THIS SHEET

1. ALL EXHAUST FAN EQUIPMENT TO BE ROUTED TO NEAREST ICP PANEL.
2. INSTALL SPOT LEAK DETECTION ON FLOOR NEAR FCA FACILITY WATER CONNECTIONS, TYPICAL.
3. INSTALL SPOT LEAK DETECTION ON FLOOR BETWEEN FCA AND WATER CONTAINMENT PLATE, TYPICAL.
4. PANEL FURNISHED BY OWNER AND INSTALLED BY CONTRACTOR.
5. FURNISHED AND INSTALLED BY CONTRACTOR.

SHEET LEGEND

(T) **TAG** DESTINATION	TEMPERATURE TRANSMITTER FURNISHED BY CONTRACTOR
(DP) **TAG** DESTINATION	DIFFERENTIAL PRESSURE TRANSMITTER FURNISHED BY CONTRACTOR
[T] **TAG** DESTINATION	TEMPERATURE TRANSMITTER/CONTROLLER FURNISHED BY EQUIPMENT VENDOR
(LD) **TAG** DESTINATION	SPOT LEAK DETECTOR FURNISHED BY CONTRACTOR 1 CCD-004
(H) **TAG** DESTINATION	HUMIDITY TRANSMITTER FURNISHED BY CONTRACTOR

KEY PLAN

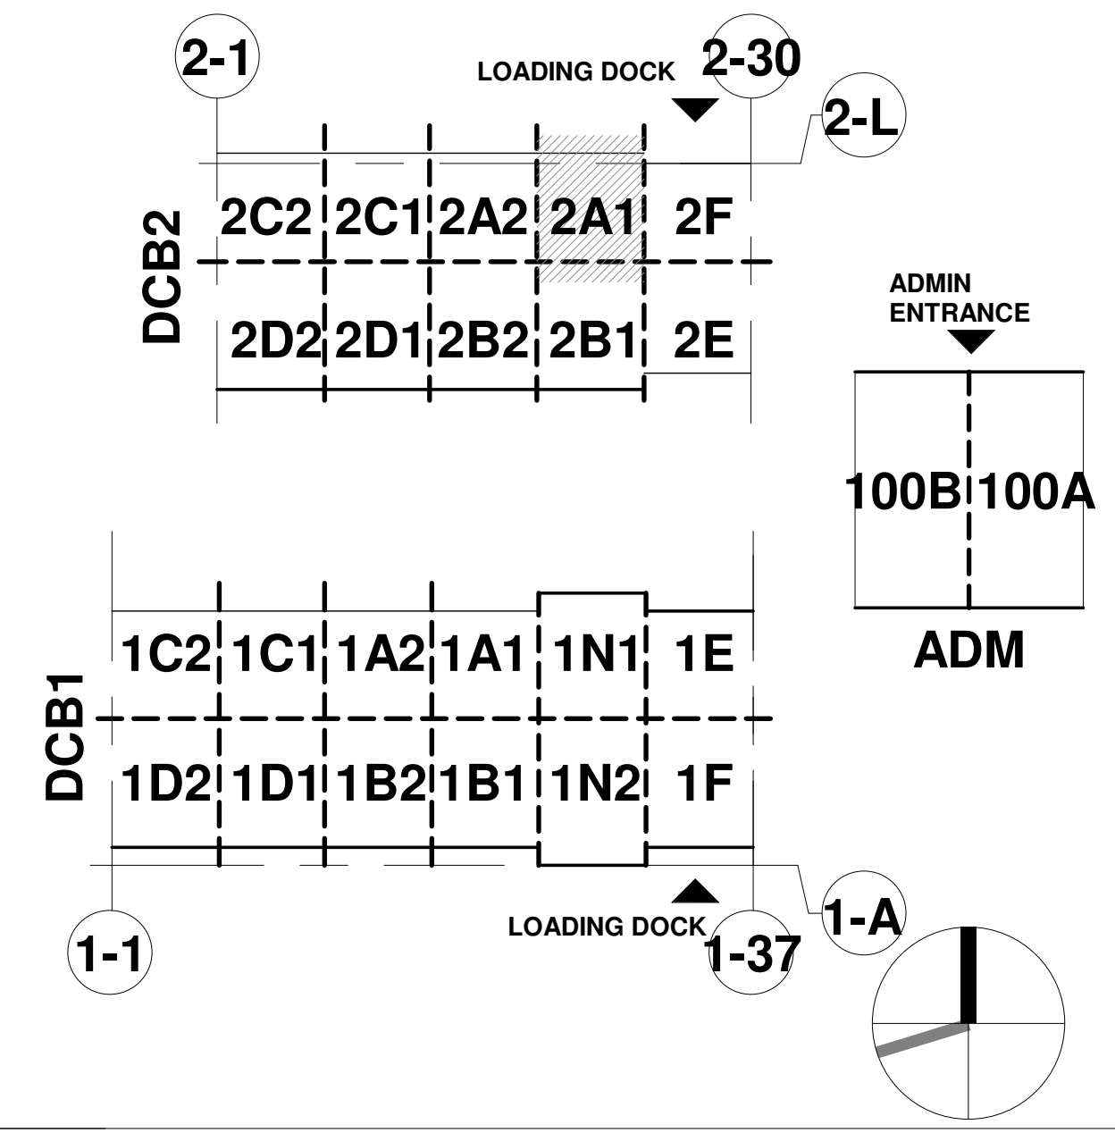

BURNS McDONNELL
FIRM REGISTRATION #: 845

Jacobs
FIRM REGISTRATION #: F2966

PEOPLES ASSOCIATES
STRUCTURAL ENGINEERS
FIRM REGISTRATION #: 18355

TEECOM
50 California Street
Suite 1500
San Francisco, CA
94111
(510) 337 2800
www.teecom.com
Firm Registration
Number: 17900

olsson
2111 S 67th Street / Suite 200 / Omaha, NE 68106
FIRM REGISTRATION #: 4523

O2
Landscape Architecture
Masterplanning
Environmental Design
115 Washington Avenue North
Suite 200
Minneapolis, MN 55410
612-359-9144
130 East Randolph Street
Suite 3100
Chicago, IL 60601
www.O2.design
MINNEAPOLIS | CHICAGO

RAS
Design Group

PROJECT ADDRESS

3101 Industrial Blvd
Temple, TX 76504

No.	Description	Date
1	INFORMATION BULLETIN 1	01/30/2024

SHEET REVISIONS

INFORMATION BULLETIN 1	01/30/2024
ISSUED FOR CONSTRUCTION PACKAGE	09/20/2023

PROJECT ISSUANCES

STATE OF TEXAS
VICTORIA ELVING
139614
LICENSED PROFESSIONAL ENGINEER
Victoria Elving
1/26/2024

PROJECT:

TTX1-2

DATA CENTER

DWG. TITLE

DCB2 -
INSTRUMENTATION
FLOOR PLAN FIRST
FLOOR AREA 2A1

PROJECT NO: 154529
DATE: JANUARY 30, 2024
SCALE:
0' 2' 4' 6' 8' 12' 16'
SCALE: 1/8" =1'-0"

DWG. NO:
IC120.1-2A1

SHEET SIZE: E (36"x48")